


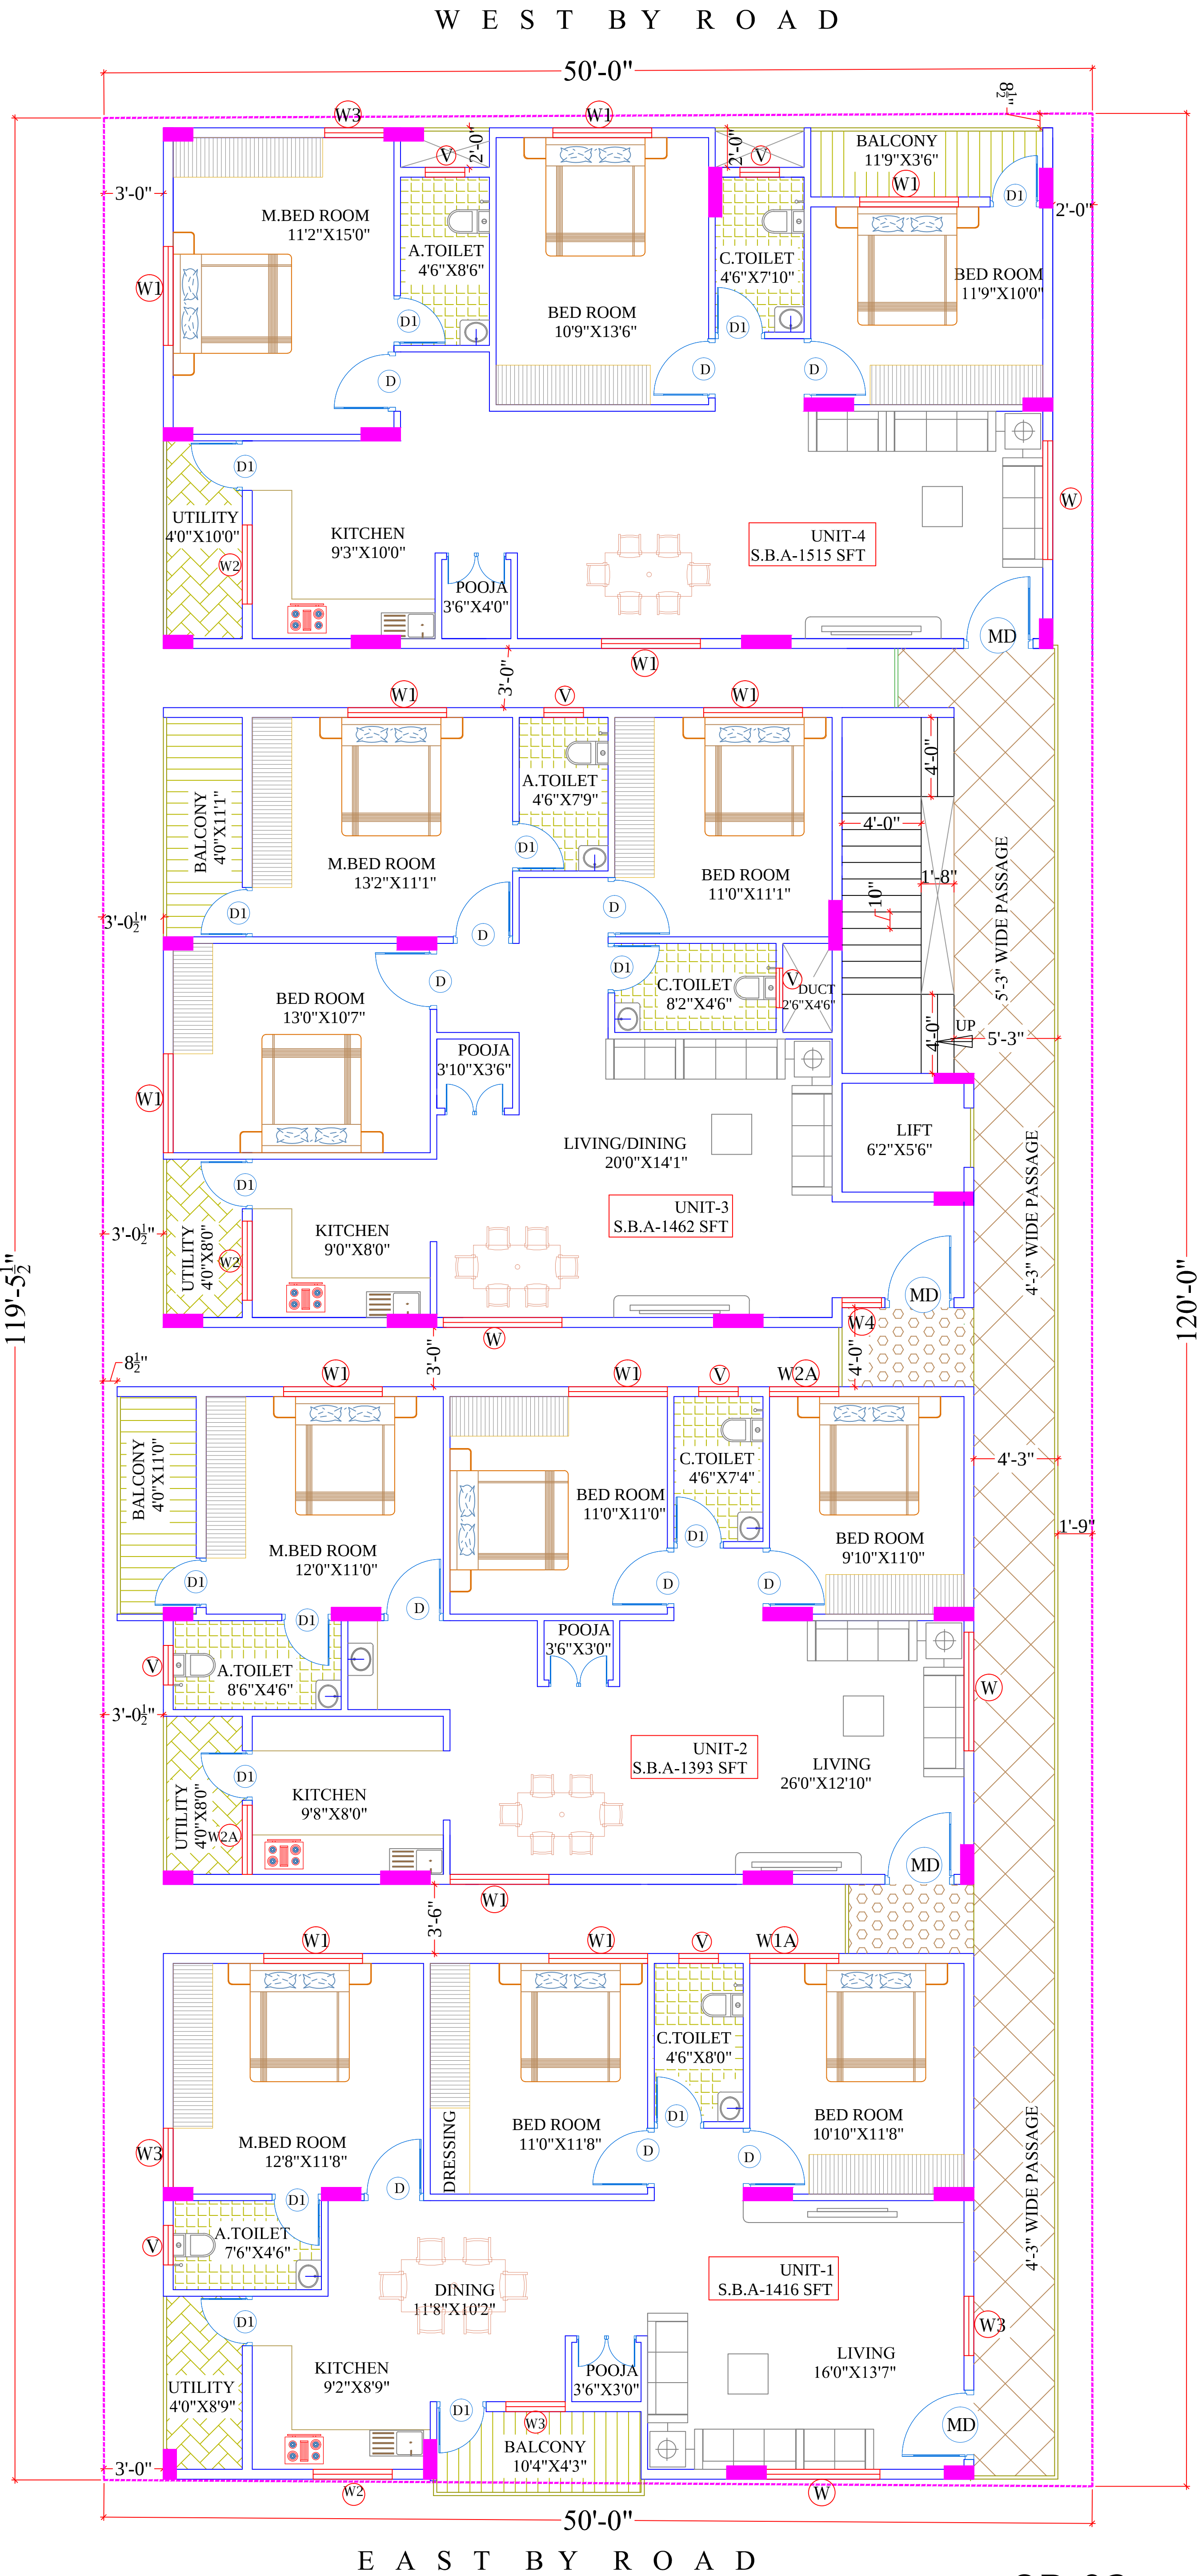

TYPICAL FLOOR PLAN

OP-02

ARCHITECT'S INSTRUCTIONS:-

- * DRAWING NOT TO BE SCALED, WRITTEN DIMENSIONS ONLY TO BE FOLLOWED.
- * CONTACT THE ARCHITECTS INCASE OF DOUBTS AND DISCREPANCIES.
- * ALL WALLS ARE 6" THICK AND PARTITION WALLS ARE 4" THICK UNLESS SPECIFIED.
- * ROOF HEIGHTS 10'-0" FROM FINISHED FLOOR LEVEL TO TOP OF ROOF SLAB UNLESS SPECIFIED.
- * ALL DIMENSIONS ARE IN FEET AND INCHES.

SL NO	DRAWING	ISSUE/ REV DATE	REV.
1	TYP.F	03.05.2022	R0

SCHEMATIC DRAWING	ORIENTATION:-
DRG NO	AR-02

PROJECT NAME AND ADDRESS:-

PROPOSED RESIDENTIAL APARTMENT
FOR "M/s.SREE SAI SINDHUJA"
@ BANGALURU.

ARCHITECTS:-

AKSHAYA CONSULTANTS

ARCHITECTURE * ENGINEERING * INTERIORS

#3/102, 2nd CROSS, 1st FLOOR, "KUSHI NILAYA".
UTTARAHALLI MAIN ROAD, BANK COLONY,
CHIKKALASANDRA POST OFFICE ROAD.
LAND MARK: OPP SHANTHI SAGAR HOTEL ROAD,
BANGALORE-560061,
PH: 080-42005228/9880005228.

E-MAIL ID:-

akshayacon9@gmail.com

TYPICAL FLOOR PLAN