


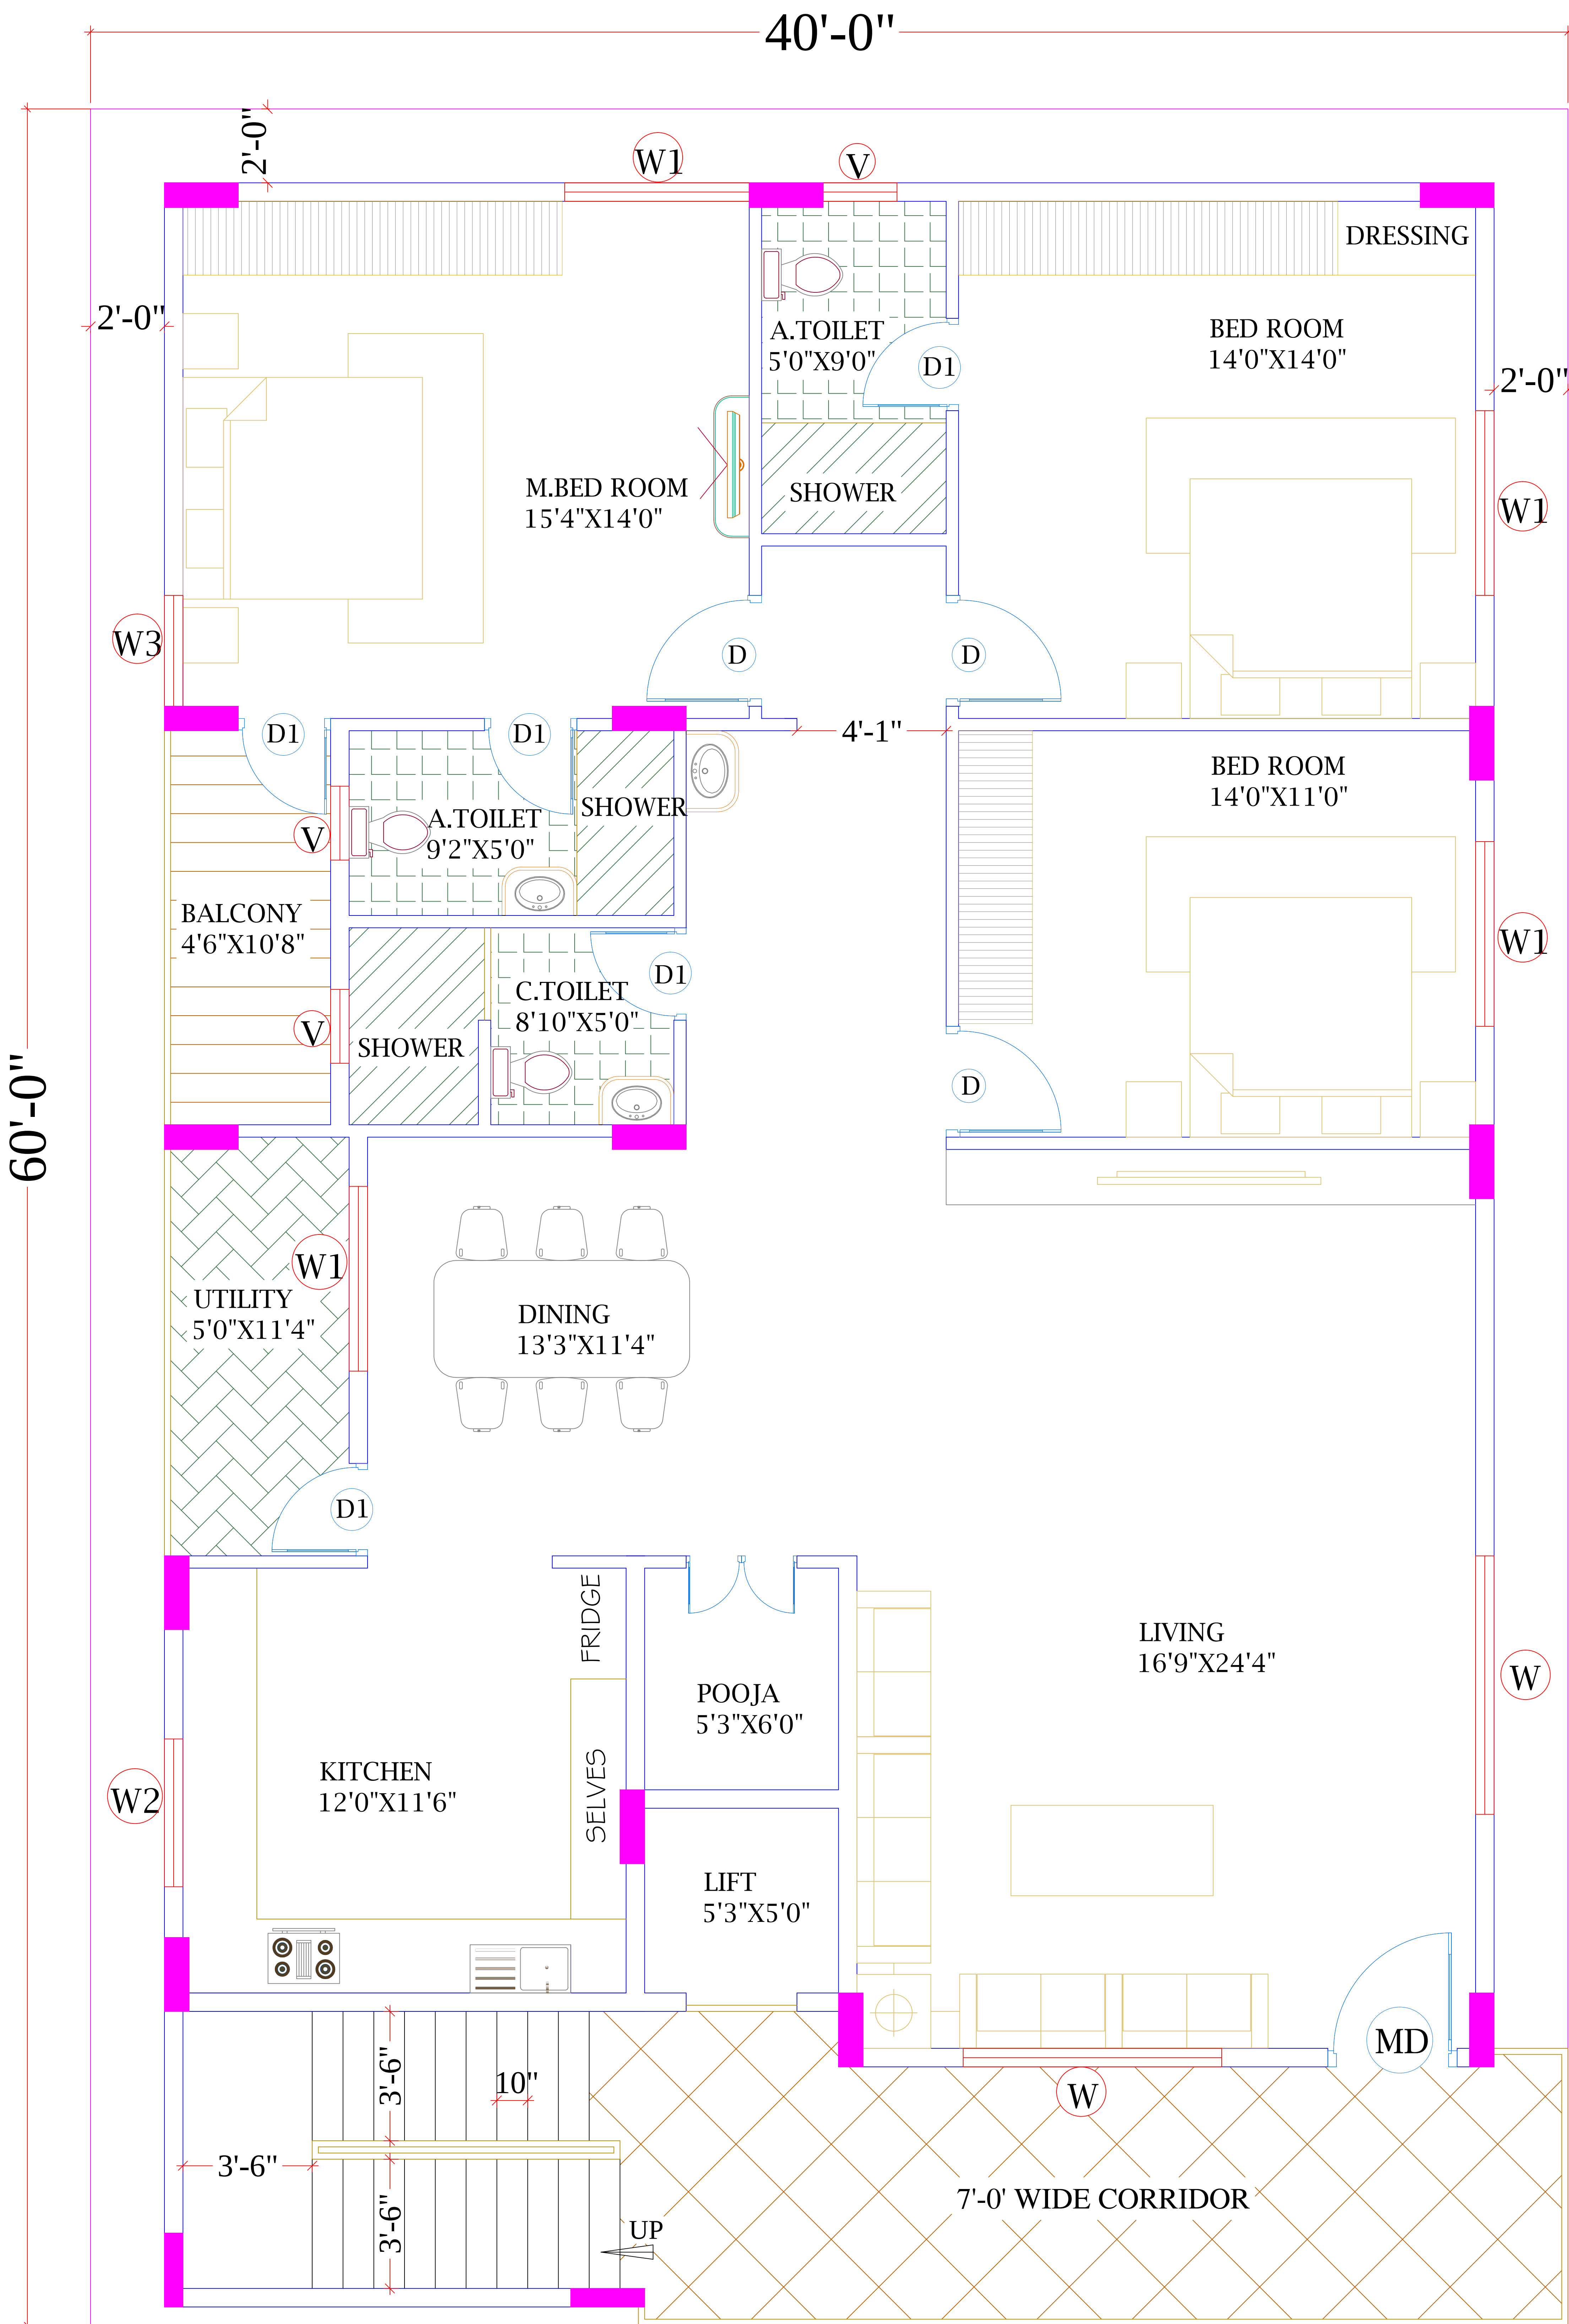

E A S T B Y R O A D

TYPICAL FLOOR PLAN(G.F,1st.F&2nd.F)

ARCHITECT'S INSTRUCTIONS:-

- * DRAWING NOT TO BE SCALED, WRITTEN DIMENSIONS ONLY TO BE FOLLOWED.
- * CONTACT THE ARCHITECTS INCASE OF DOUBTS AND DISCREPANCIES.
- * ALL WALLS ARE 6" THICK AND PARTITION WALLS ARE 4" THICK UNLESS SPECIFIED.
- * ROOF HEIGHTS 10'-6" FROM FINISHED FLOOR LEVEL TO TOP OF ROOF SLAB UNLESS SPECIFIED.
- * ALL DIMENSIONS ARE IN FEET AND INCHES.

SL NO	DRAWING	ISSUE/ REV DATE	REV.
1	TYP.F	08.11.2022	R2

SCHEMATIC DRAWING

ORIENTATION:-

DRG,NO: AR-02

PROJECT NAME AND ADDRESS:-

PROPOSED RESIDENTIAL BUILDING FOR
Mr.BHASKAR NAIDU,
@ BANGALURU.

AKSHAYA CONSULTANTS

ARCHITECTURE * ENGINEERING * INTERIORS

#3/102, 2nd CROSS, 1st FLOOR, "KUSHI NILAYA".
UTTHARAHALLI MAIN ROAD, BANK COLONY,
CHIKKALASANDRA POST OFFICE ROAD.
LAND MARK: OPP SHANTHI SAGAR HOTEL ROAD,
BANGLORE-560061,
PH: 080-42005228/9880005228.

E-MAIL ID:-

akshayacon9@gmail.com

TYPICAL FLOOR PLAN